

SUPPLY SCOPE: Nudura ICF forms, accessories, pre-cut service, alignment hire and haulage as the quotation only. ENGLAND - Building Regulations. Ridge ~10.1 m, below 11 m. Floors, steels, stairs, roofs, windows and timber partitions are shown in good faith for coordination only - engineer / specialists to design.

QUOTATION - NOT FOR CONSTRUCTION

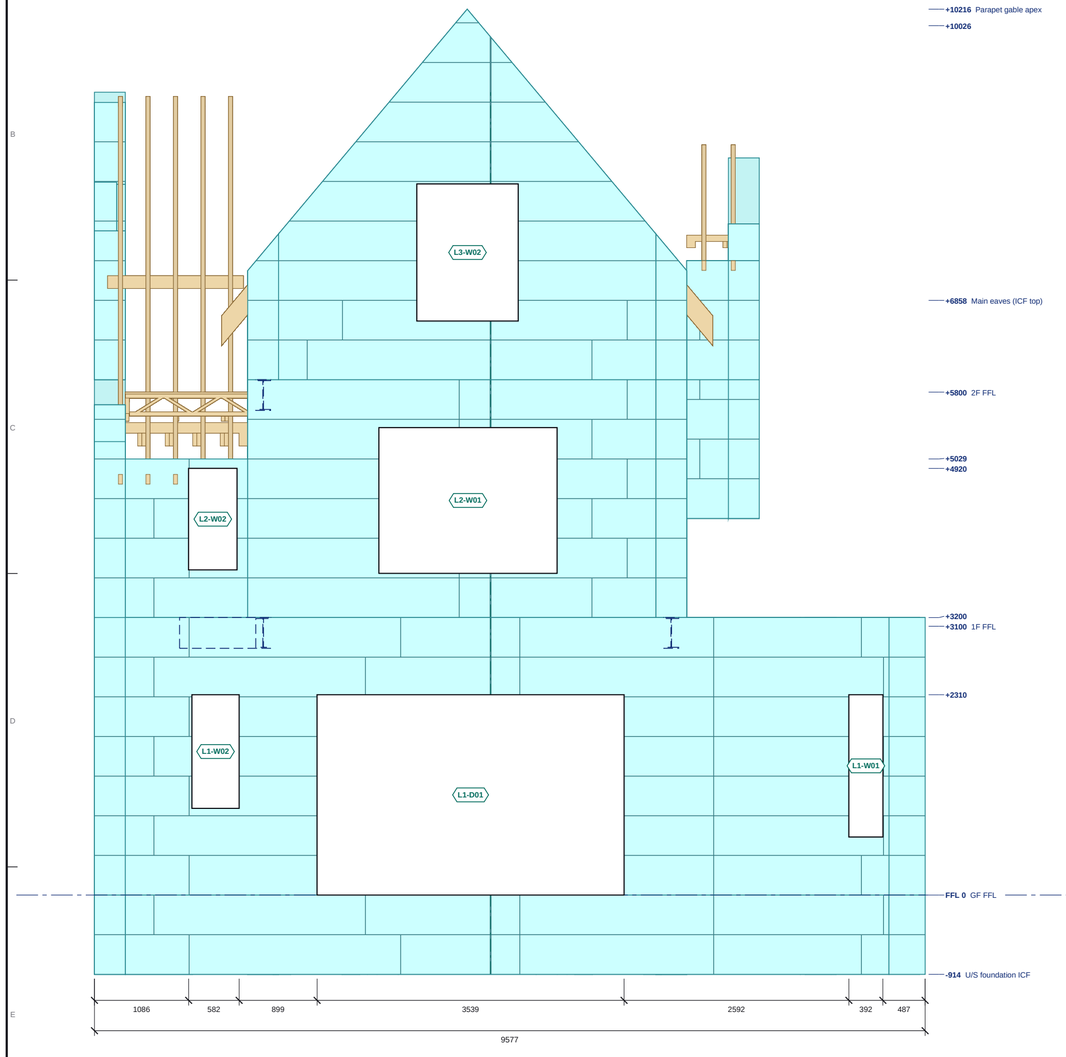

NORTH ELEVATION

Scale 1:50 @ A2 | Levels above GF FFL; sills and heads in the schedule

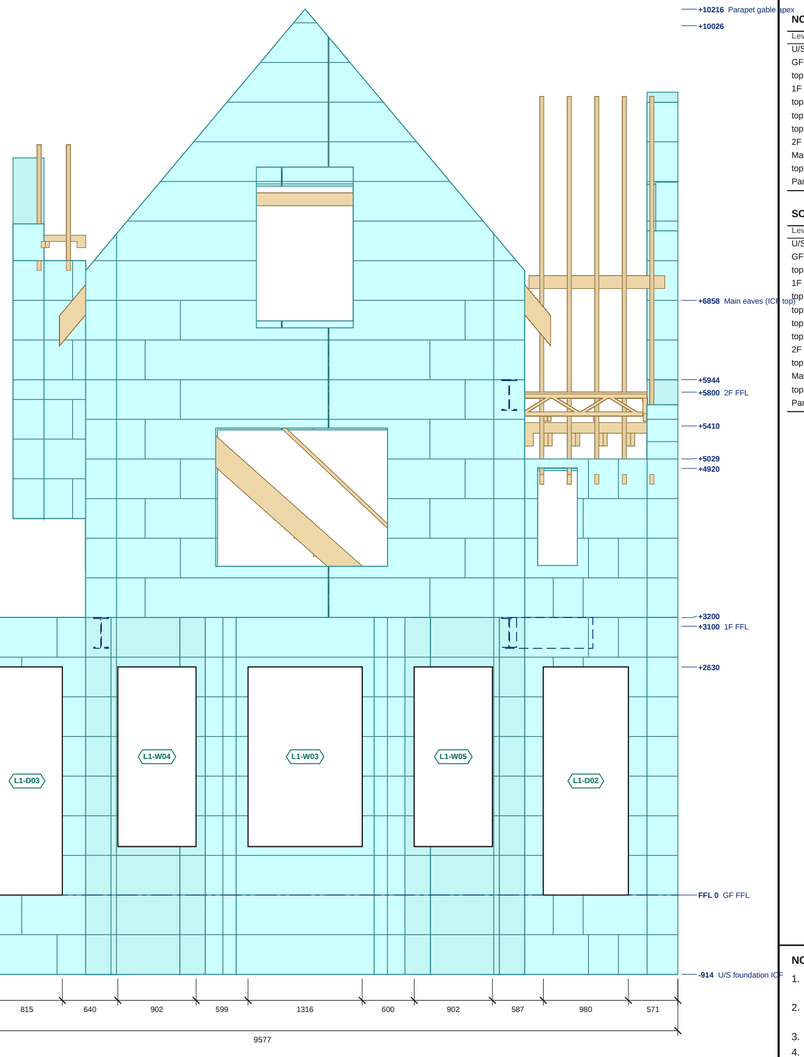

SOUTH ELEVATION

Scale 1:50 @ A2 | Levels above GF FFL; sills and heads in the schedule

0 1 2 3m

ICF external EPS face
Block course joint
Stack joint
Steel
Roof build-up (slab / earth / sedum)
GF slab + foundation build-up, ACO

ELEVATION SCHEDULES

NORTH ELEVATION: OPENINGS

Ref	Width	Height	Sill	Head	Lintel
L1-W01	392	1640	+670	+2310	-
L1-D01	3538	2310	0	+2310	-
L1-W02	543	1310	+1000	+2310	-
L2-W01	2053	1680	+3710	+5390	-
L2-W02	557	1170	+3750	+4920	-
L3-W02	1168	1580	+6620	+8200	-

Structural openings in the ICF; sill and head above GF FFL.

SOUTH ELEVATION: OPENINGS

Ref	Width	Height	Sill	Head	Lintel
L1-W03	1316	2070	+560	+2630	-
L1-W04	850	2070	+560	+2630	-
L1-W05	850	2070	+560	+2630	-
L1-D02	980	2630	0	+2630	-
L1-D03	815	2630	0	+2630	-

Structural openings in the ICF; sill and head above GF FFL.

NORTH ELEVATION: LEVELS

Level	FFL
U/S foundation ICF	-914
GF FFL	0
top of ICF	+2310
1F FFL	+3100
top of ICF	+3200
top of ICF	+4920
top of ICF	+5029
2F FFL	+5800
Main eaves (ICF top)	+6858
top of roof build-up	+10026
Parapet gable apex	+10216

SOUTH ELEVATION: LEVELS

Level	FFL
U/S foundation ICF	-914
GF FFL	0
top of ICF	+2630
1F FFL	+3100
top of ICF	+3200
top of ICF	+4920
top of ICF	+5029
top of ICF	+5410
2F FFL	+5800
top of ICF	+5944
Main eaves (ICF top)	+6858
top of roof build-up	+10026
Parapet gable apex	+10216

NOTES

1. ICF: Nudura 6" XR35, 101.6 EPS + 152.4 core + 101.6 EPS = 355.6. External EPS face shown with the block course joints, vertical block joints and stack joints as populated.
2. Levels above GF FFL. Openings are structural openings in the ICF; glazing, doors, render and finishes by others, not shown.
3. Steel, roof build-up and ground floor build-up shown as modelled.
4. See ES26-065-GA-01 for plan setting out, lintels and steel.

REVISIONS

REV	DATE	DESCRIPTION
-	02.11.26	Quotation issue

Nudura™ BuildEase

CLIENT	PROJECT
Cuckfield Real Estate Ltd	Clifton College Garage Site, Clifton Park Road, Bristol

DRAWING TITLE
NORTH AND SOUTH ELEVATIONS
ICF elevations with openings, levels and roof build-up

SCALE	SIZE	DATE
1:50	A2	02.11.26
DRAWN	CHECKED	APPROVED
TS		

STATUS	DRAWING No.	REV
QUOTATION	ES26-065-EL-01	-

Do not scale. All dimensions in millimetres, levels in metres from GF FFL. Check all dimensions on site.