
SUPPLY SCOPE: Nudura ICF forms, accessories, pre-cut service, alignment hire and haulage as the quotation only. ENGLAND - Building Regulations. Ridge ~10.1 m, below 11 m. Floors, steels, stairs, roofs, windows and timber partitions are shown in good faith for coordination only - engineer / specialists to design.

QUOTATION - NOT FOR CONSTRUCTION

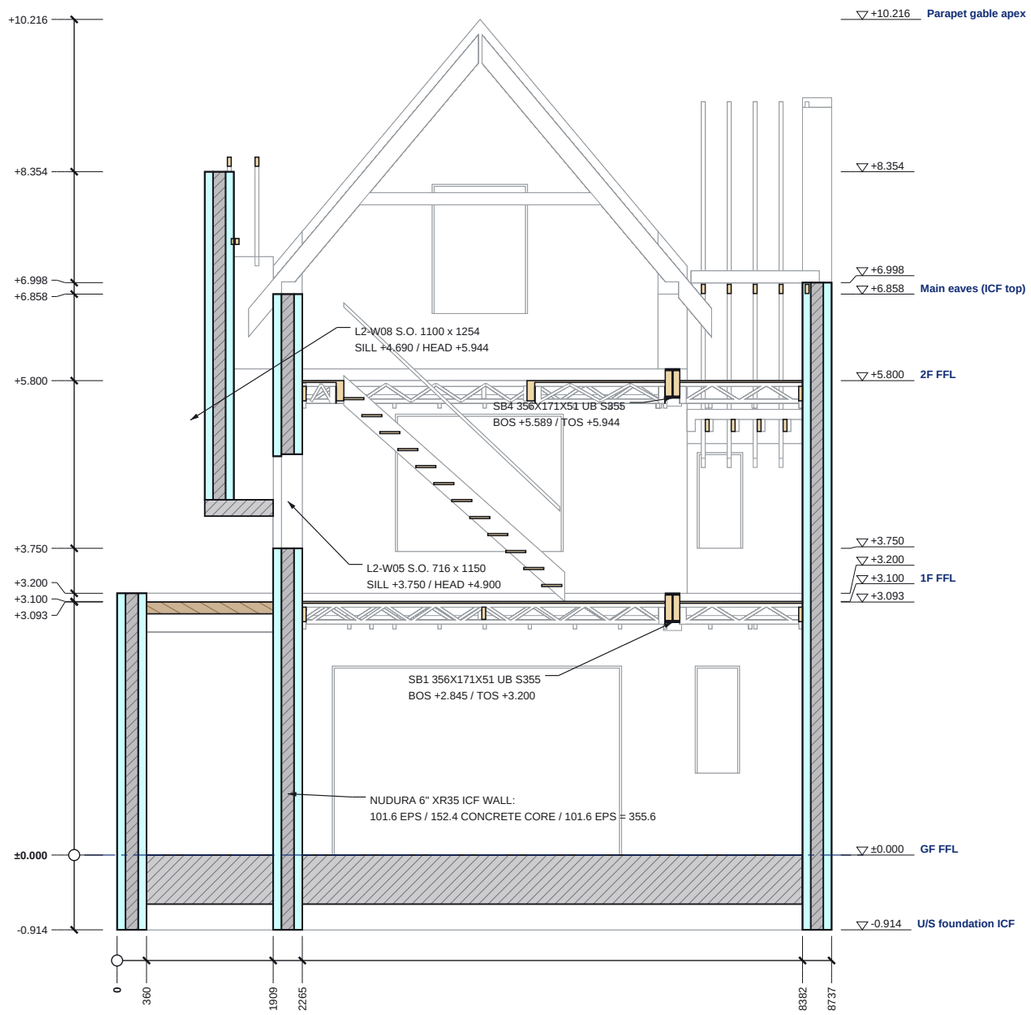

SECTION A-A

Scale 1:75 @ A3 | Looking north; levels above GF FFL

ICF EPS (cut)
ICF concrete core / RC (cut)
Steel (cut)
Blinding / hardcore
Beyond the cut (line work)

0 1 2 3 4m

Do not scale. All dimensions in millimetres, levels in metres from GF FFL. Check all dimensions on site.

SECTION A-A SCHEDULES


LEVELS ON THIS SECTION

Level	FFL
U/S foundation ICF	-0.914
GF FFL	±0.000
top of roof build-up	+3.093
1F FFL	+3.100
top of ICF W10	+3.200
top of ICF W12	+3.750
2F FFL	+5.800
Main eaves (ICF top)	+6.858
top of ICF W06	+6.998
top of ICF W09	+8.354
Parapet gable apex	+10.216

STEEL CUT BY THIS SECTION

Mark	Section (engineer)	BOS	TOS
SB1	356x171x51 UB S355	+2.845	+3.200
SB4	356x171x51 UB S355	+5.589	+5.944

SECTION KEY

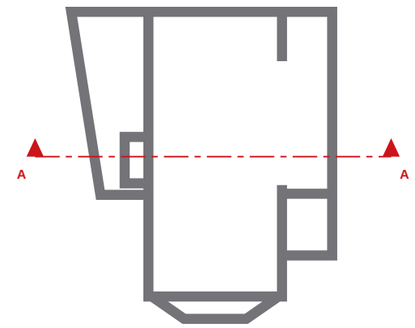

NOTES

1. Section A-A is a BuildEase ICF section (not an architect's section line). Cut elements hatched / filled; the model beyond the cut in line work.
2. Levels above GF FFL.
3. ICF: Nudura 6" XR35, 101.6 EPS + 152.4 core + 101.6 EPS = 355.6, 152.4 core + 101.6 EPS = 355.6. No structural design yet (planning drawings). ICF per the quotation model: 6in XR35 throughout with the Nudura Brick Ledge on the foundation course (natural stone outer leaf), 2-course foundation on a strip footing (by others), internal load-bearing walls in ICF, front / rear parapet gables and the wing gable raked to the 50 degree roof, the oriel on an RC corbel. Floor steels, corbel, roof and stairs indicative - engineer.
4. Steel marks, BOS / TOS: rev -. See ES26-065-GA-01 / EL-01 / EL-02 in the approval drawings pack.

REVISIONS

REV	DATE	DESCRIPTION
-	02.11.26	Quotation issue

Nudura™ BuildEase

CLIENT	PROJECT
Cuckfield Real Estate Ltd	Clifton College Garage Site, Clifton Park Road, Bristol

DRAWING TITLE
SECTION A-A
ICF section with levels and build-ups

SCALE	SIZE	DATE
1:75	A3	02.11.26
DRAWN	CHECKED	APPROVED
TS		

STATUS	DRAWING No.	REV
QUOTATION	ES26-065-SE-01	-