SUPPLY SCOPE: Nudura ICF forms, accessories, pre-cut service, alignment hire and haulage as the quotation only. ENGLAND - Building Regulations. Ridge ~10.1 m, below 11 m. Floors, steels, stairs, roofs, windows and timber partitions are shown in good faith for coordination only - engineer / specialists to design.

QUOTATION - NOT FOR CONSTRUCTION

ASSUMED - NOT MODELLED (BOQ allowance)

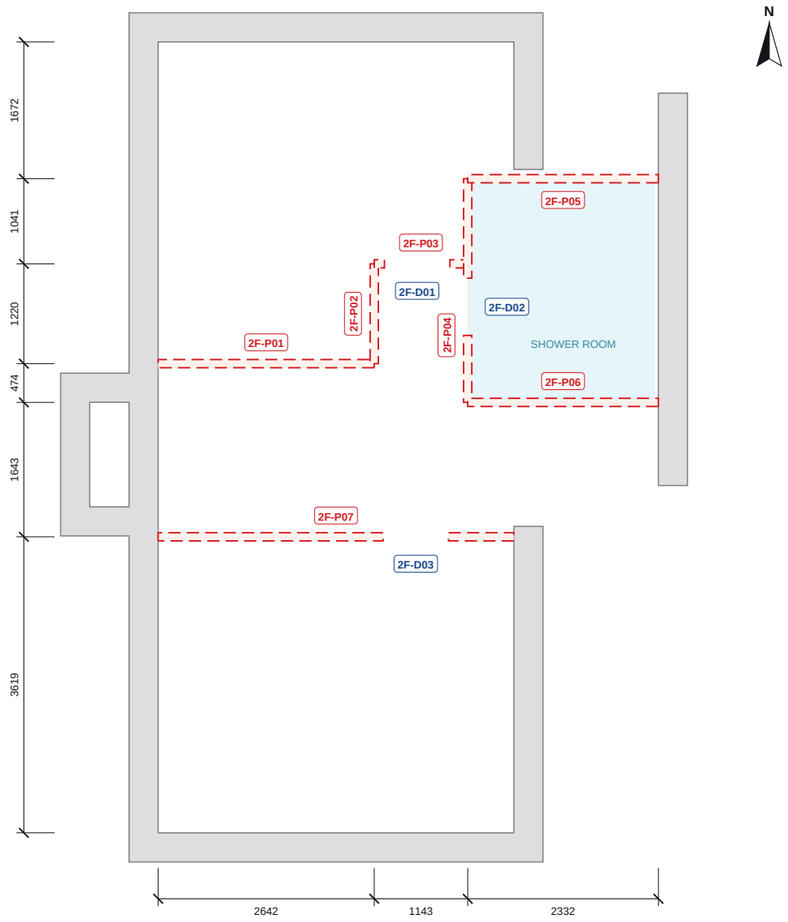

SOUTH (front, Clifton Park Road)

SECOND FLOOR PARTITIONS (ASSUMED) PLAN

Scale 1:75 @ A3 | ICF cut at +6,400 (600 above 2F FFL)

0 1 2 3 4 5m

Assumed partition (not modelled)

Wet room (shower room)

Nudura ICF (context only)

SECOND FLOOR SCHEDULES (ASSUMED)

PARTITION SCHEDULE (ASSUMED)

Wall	Length	Studs	Between
2F-P01	2,642	@600	bed 4 / stair
2F-P02	1,220	@600	bed 4 / landing
2F-P03	1,143	@600	bed 4 door wall
2F-P04	2,735	@400 wet	landing / shower room
2F-P05	2,332	@400 wet	shower room north
2F-P06	2,332	@400 wet	shower room south
2F-P07	4,350	@600	bed 3 / landing
Total	**16,754**		**7 partitions**

Lengths along the centre line from the spec.

DOOR OPENINGS (ASSUMED)

Door	Wall	Width	Note
2F-D01	2F-P03	800	bed 4
2F-D02	2F-P04	700	shower room
2F-D03	2F-P07	800	bed 3

NOTES

1. ASSUMPTION - NOT MODELLED: the second-floor rooms sit under the 50 deg roof and their partitions are not in the quotation model. They are drawn here dashed from the planning plans (O'Leary Goss PA112 D) for the BOQ allowance only: 7 partitions, 16.8 m run, 3 doors.
2. Assumed build-up as GF / 1F: 38x89 C16 studs @600 (@400 on the shower-room walls), rails, noggins, 15 plasterboard each side; heads RAKED to the rafter / ceiling line where under the slope (frame to suit on site).
3. Base = 2F FFL +5,800 on the PS10 deck (ES26-065-FL-03). Heads raked to the rafter soffits, flat under the main-roof collar ceiling at +7,950 (raised ties, ES26-065-RF-01).
4. Set-out dimensions to partition centre lines as read off the planning plans; check on site.

REVISIONS

REV	DATE	DESCRIPTION
-	02.11.26	Quotation issue

Nudura™ BuildEase

CLIENT	PROJECT
Cuckfield Real Estate Ltd	Clifton College Garage Site, Clifton Park Road, Bristol

DRAWING TITLE

SECOND FLOOR PARTITIONS (ASSUMED)

Assumed 2F partitions (not modelled) - BOQ allowance

SCALE	SIZE	DATE
AS SHOWN	A3	02.11.26
DRAWN	**CHECKED**	**APPROVED**
TS		

STATUS	DRAWING No.	REV
QUOTATION	ES26-065-TF-03	-

Do not scale. All dimensions in mm. Check all dimensions on site.