
SUPPLY SCOPE: Nudura ICF forms, accessories, pre-cut service, alignment hire and haulage as the quotation only. ENGLAND - Building Regulations. Ridge ~10.1 m, below 11 m. Floors, steels, stairs, roofs, windows and timber partitions are shown in good faith for coordination only - engineer / specialists to design.

QUOTATION - NOT FOR CONSTRUCTION

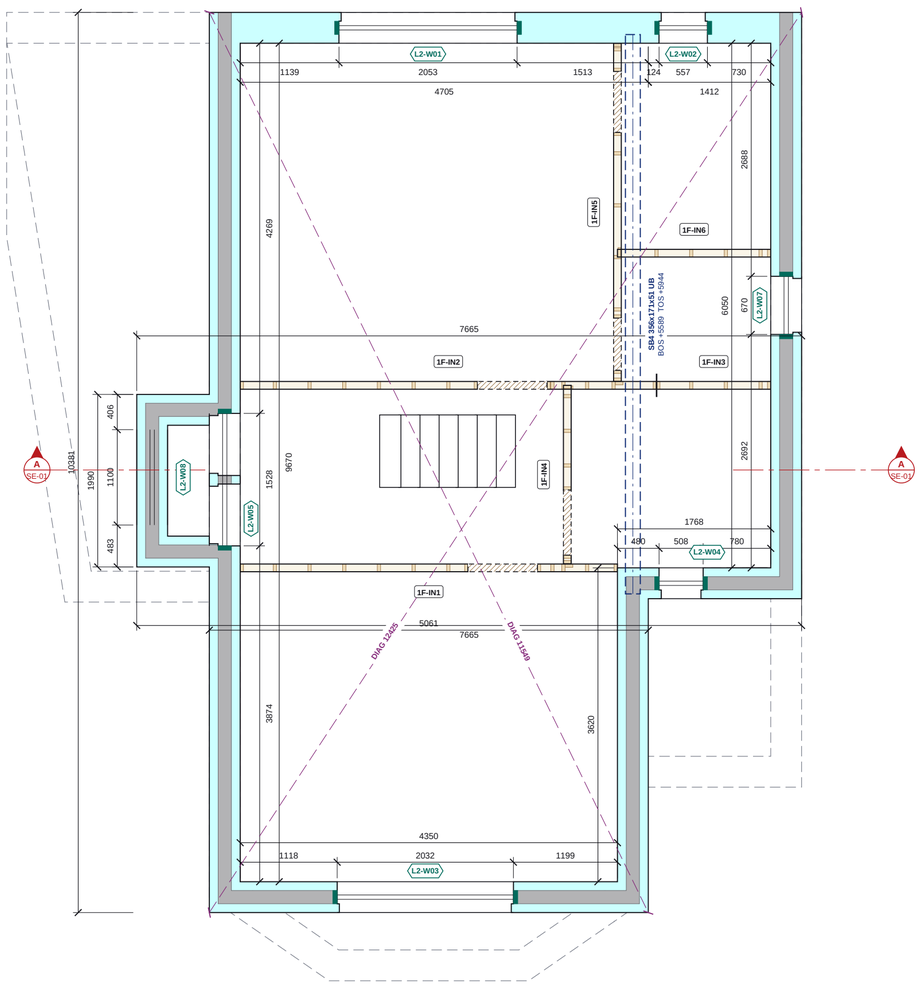

- EPS insulation (Nudura form)
- Concrete core
- End cap at opening
- Timber frame partition panel, studs cut at plan level
- Panel joint
- Door opening in a timber partition (hatched through the door, head over dashed)
- ICF walls of the level below (dashed)
- Steel over (dashed), marked
- Engineer's pier bars (n-H12 vertical bars in ICF pier) / WS wall starters
- Setting-out check diagonal (external ICF corners)
- Section line (see SE sheet)

FIRST FLOOR ICF PLAN

Scale 1:50 @ A2 | Plan cut at +4572

0 1 2 3m

FIRST FLOOR ICF SCHEDULES

OPENING SCHEDULE

Ref	Width	Height	Sill	Head	Lintel
L2-W01	2053	1680	+3710	+5390	-
L2-W02	557	1170	+3750	+4920	-
L2-W03	2032	1620	+3790	+5410	-
L2-W04	508	1150	+3800	+4950	-
L2-W07	670	1100	+3800	+4900	-
L2-W05	1528	800	+3300	+4100	-
L2-W08	1100	920	+5062	+5982	-

Structural openings in the ICF; sill and head above GF FFL.

STEEL SCHEDULE

Mark	Section (engineer)	BOS	TOS
SB4	356x171x51 UB S355	+5589	+5944

BOS / TOS = bottom / top of steel above GF FFL (C-1 columns: base / top).

NOTES

1. ICF: Nudura 6" XR35, 101.6 EPS + 152.4 core + 101.6 EPS = 355.6. Dimensions to the ICF faces.
2. Levels above GF FFL. Sill / head = structural opening in the ICF.
3. No structural design yet (planning drawings). ICF per the quotation model: 6in XR35 throughout with the Nudura Brick Ledge on the foundation course (natural stone outer leaf), 2-course foundation on a strip footing (by others), internal load-bearing walls in ICF, front / rear parapet gables and the wing gable raked to the 50 degree roof, the oriel on an RC corbel. Floor steels, corbel, roof and stairs indicative - engineer.
4. Lintel (L-n) and steel (B-n, C-1) marks from rev -, which takes precedence.
5. Masonry walls shown for context.
6. Steel over dashed. BOS / TOS = bottom / top of steel above GF FFL.

REVISIONS

REV	DATE	DESCRIPTION
-	02.11.26	Quotation issue

Nudura™ BuildEase

CLIENT	PROJECT
Cuckfield Real Estate Ltd	Clifton College Garage Site, Clifton Park Road, Bristol

DRAWING TITLE

FIRST FLOOR ICF GENERAL ARRANGEMENT

ICF walls, openings, lintels, steel over and engineer's notes

SCALE	SIZE	DATE
1:50	A2	02.11.26
DRAWN	CHECKED	APPROVED
TS		
STATUS	DRAWING No.	REV
QUOTATION	ES26-065-GA-03	-

Do not scale. All dimensions in millimetres, levels in metres from GF FFL. Check all dimensions on site.